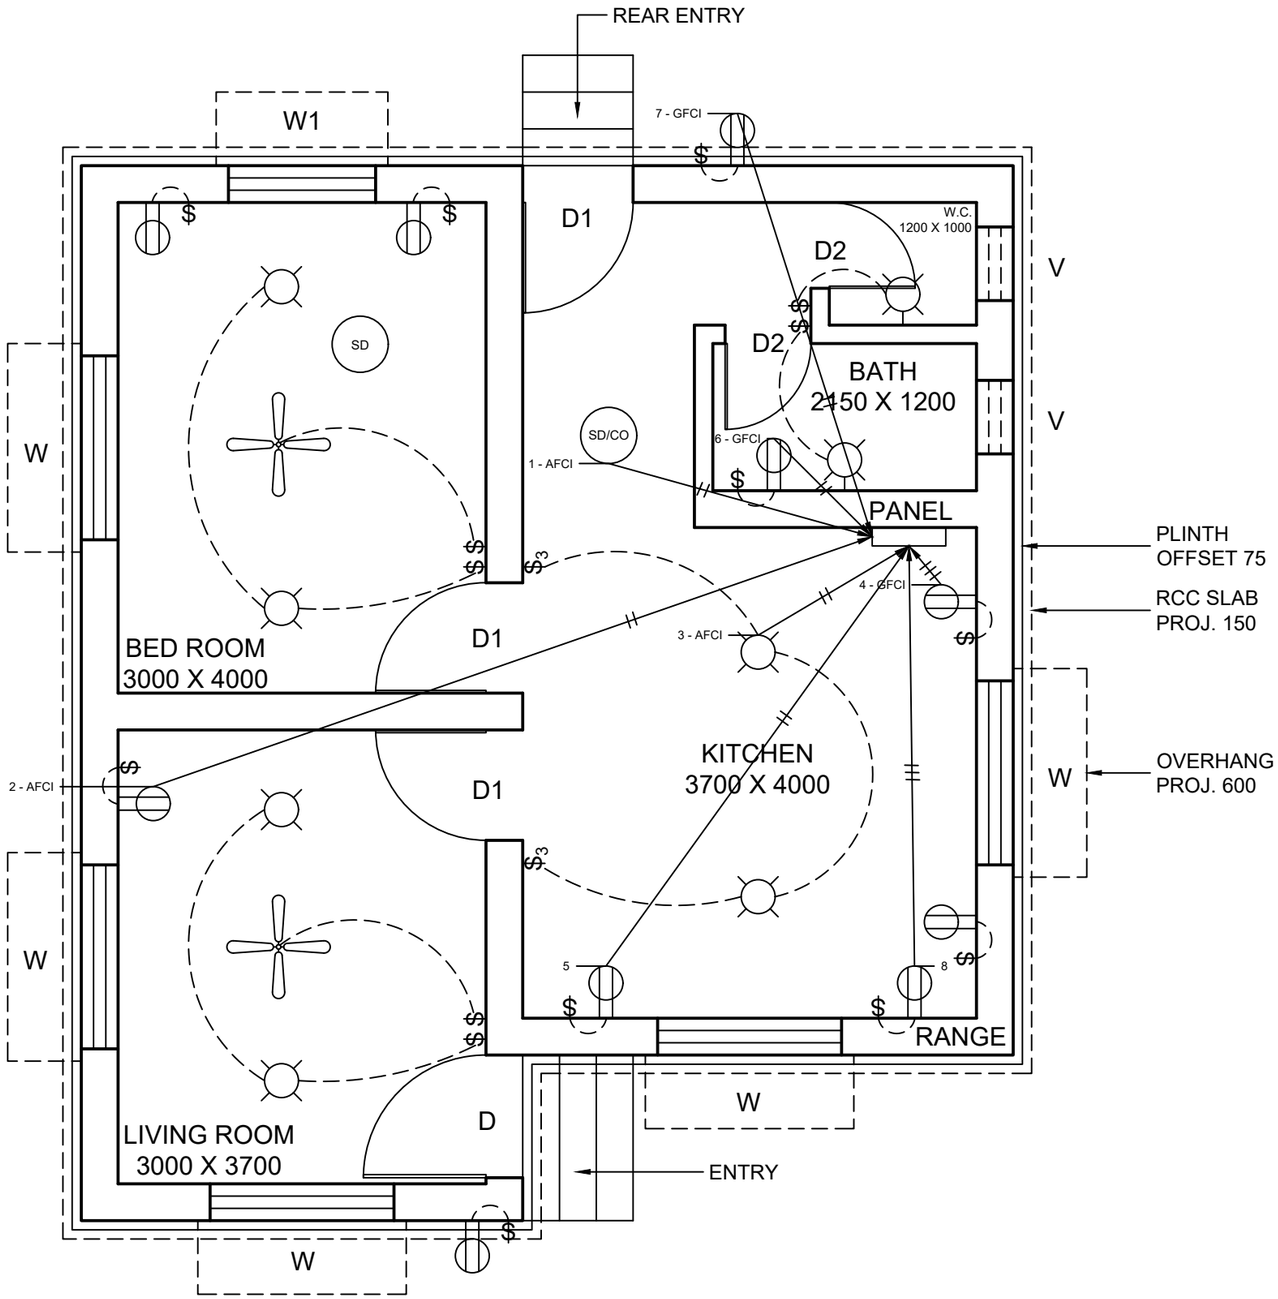


General Notes:

- Designed to CSA C22.1 (Canadian Electrical Code)
- Receptacles near sinks and outdoors are GFCI protected
- Living-area receptacle circuits are AFCI protected
- Smoke/CO detectors hardwired and interconnected
- All dimensions in mm

Symbol Legend	
Symbol	Meaning
Circle + X	Ceiling Light
Circle + Fan Blades	Ceiling Fan
Circle + Two Lines	Receptacle (Outlet)
S	Switch
S_3	3-way Switch
SD	Smoke Detector
SD/CO	Smoke + CO Detector
Arrow to Panel	Homerun to Panel
// Ticks	Number of Conductors
PANEL Box	Distribution Panel

Project: Residential Electrical Design
Drawn by: Mayan Saravanabavan
Scale: 1:50
Sheet: E-1